


DOOR SCHEDULE

- ① EXISTING
3'-0" x 7'-0"
HOLLOW METAL
- ② EXISTING 3'-0"
x 6'-0" SOLID
CORE WOOD
- ③ EXISTING 3'-0"
x 6'-0" HOLLOW
CORE WOOD
- ④ NEW 3' x 6'
SOLID CORE
WOOD DOOR
(PRE-FINISHED)
W/ "TIMELY"
PREFINISHED
METAL FRAME
- ⑤ 12'-0" x 12'-0"
STEEL ROLL-
UP DOOR.
(EXISTING)
- ⑥ EXIT SIGN 1'-
6"

EXISTING PAVED EQUIPMENT
STORAGE YARD

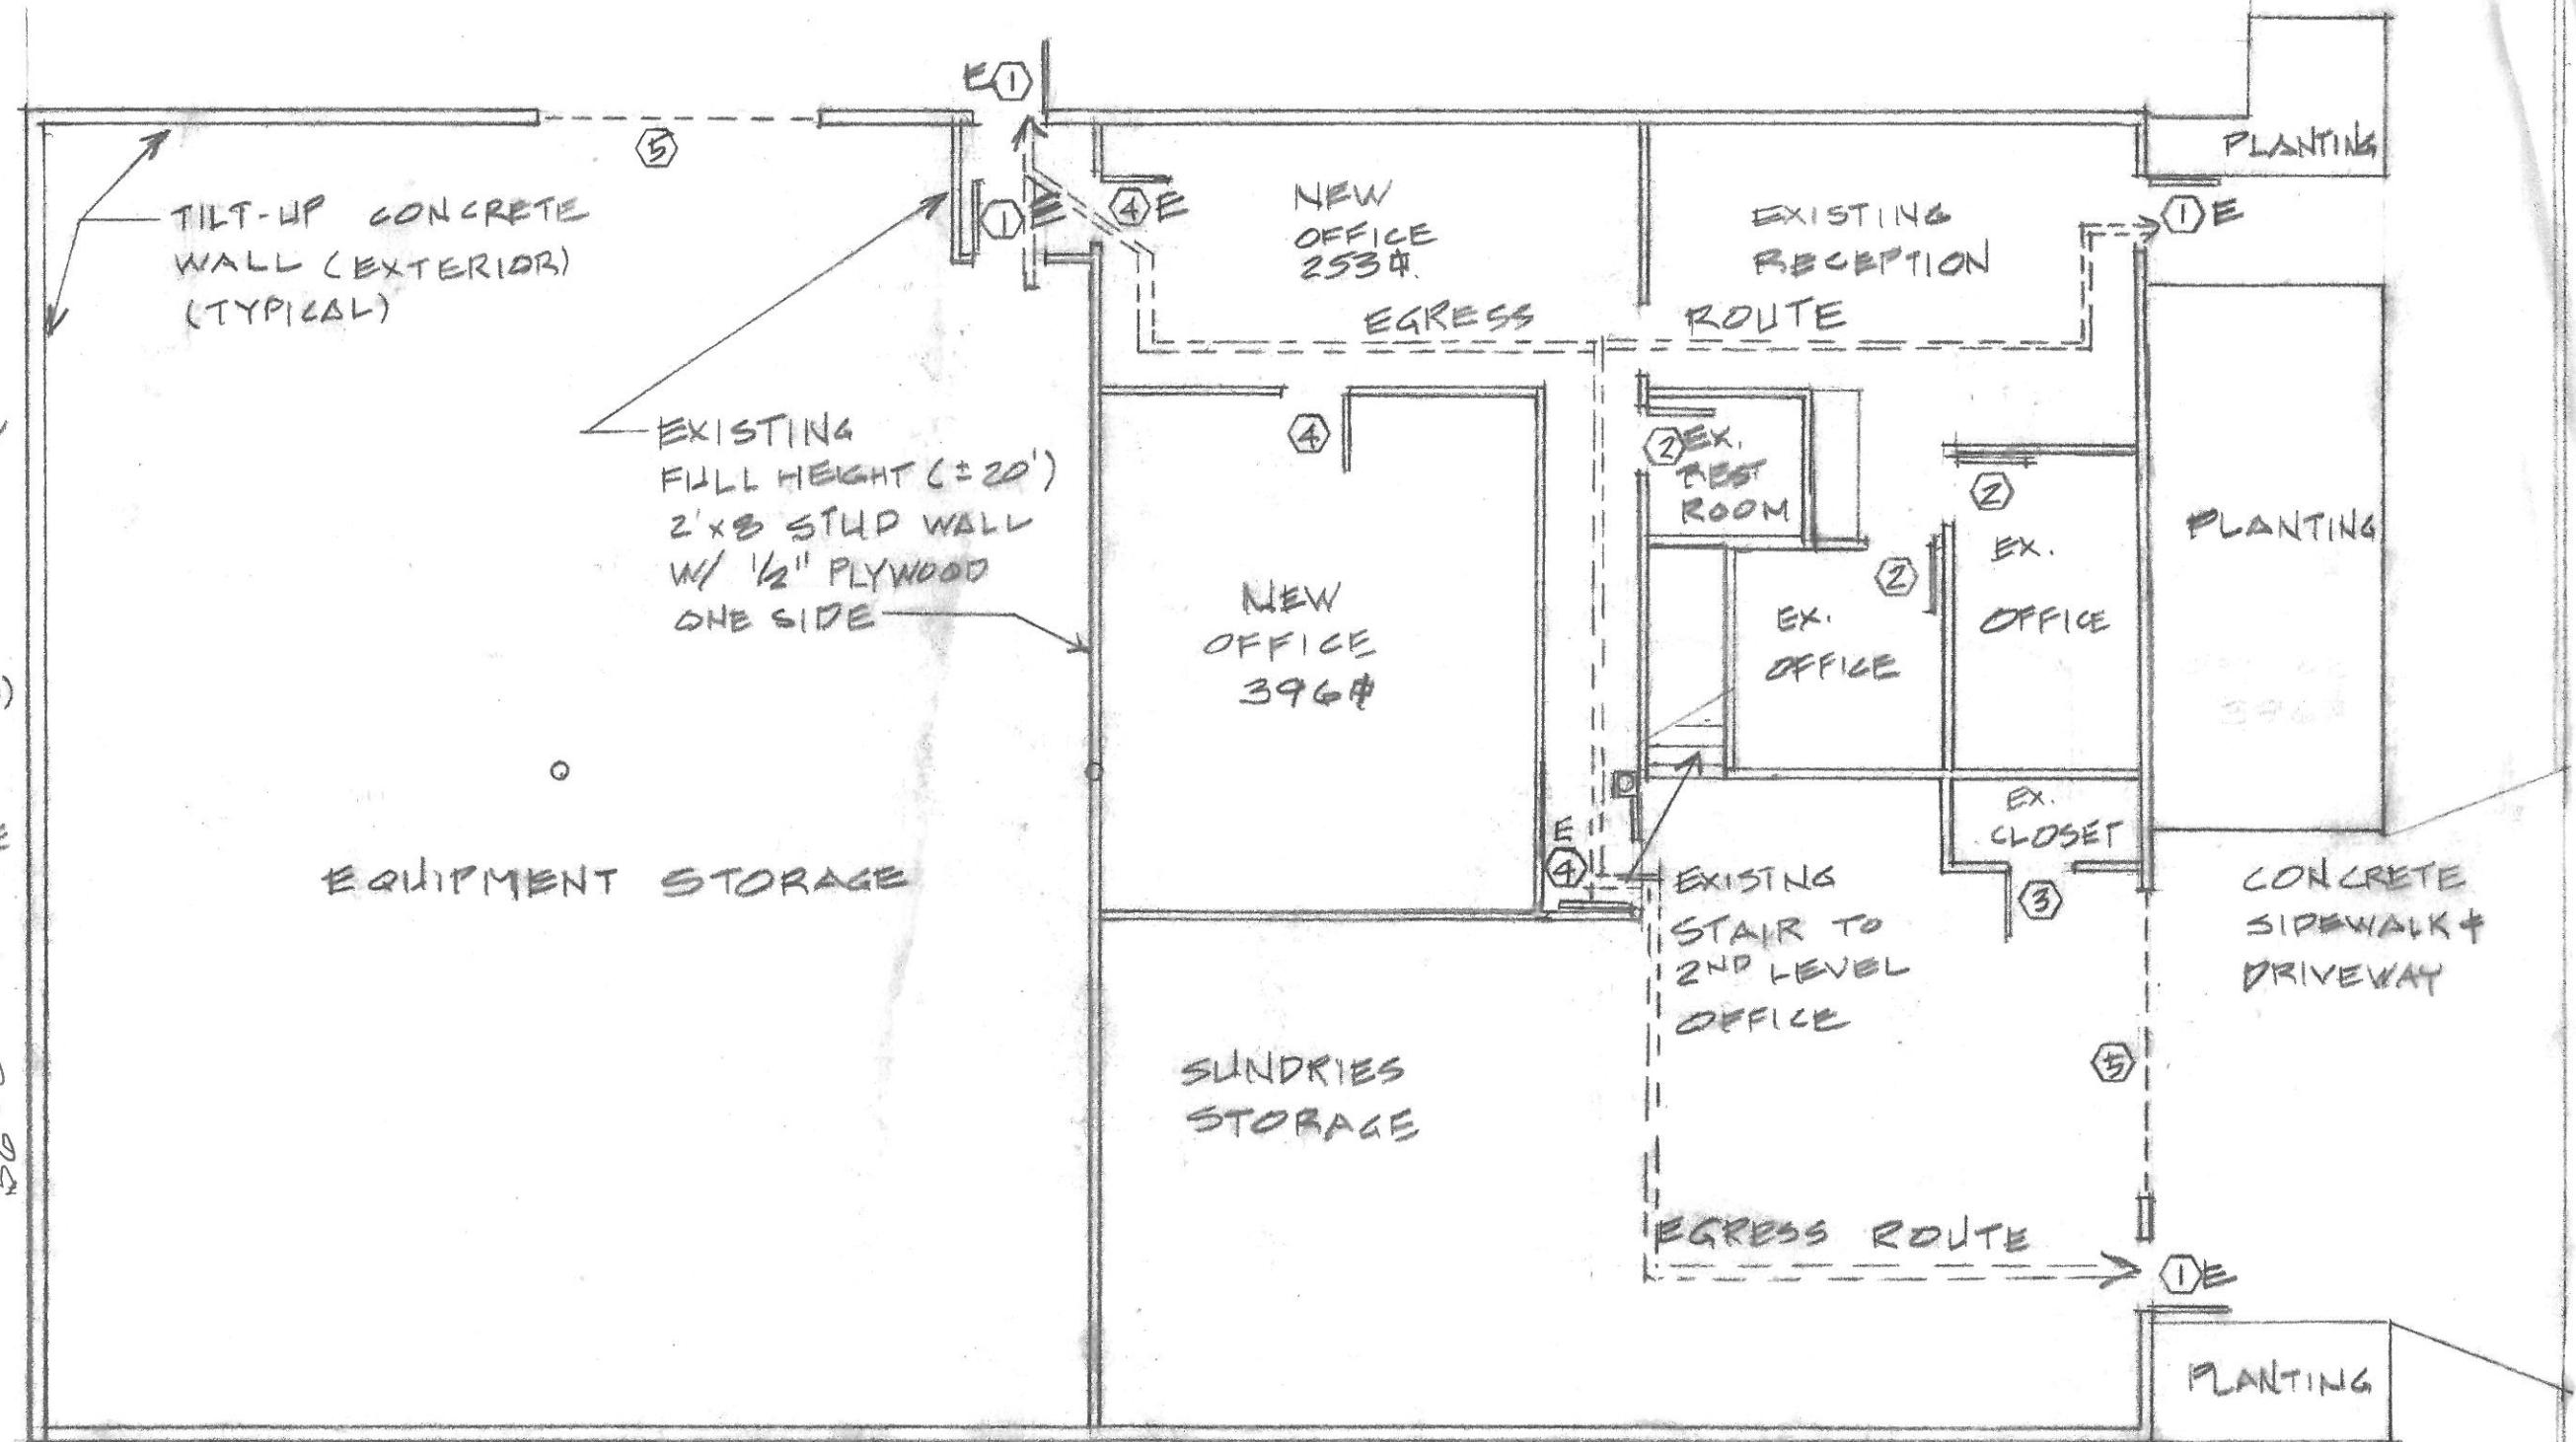

FLOOR PLAN

$\frac{1}{8}'' = 1'-0''$

90'-0"

NORTH

HANDICAP ACCESS CURB CUT

